

PORTFOLIO

RUSLAN OVEZOV

Architect | Architectural Visualizer | 3D Artist

Selected architectural visualization works

Exterior renders | Interior renders | Lighting | Post-production

Lublin, Poland

+48 789 607 914

architectruslann@gmail.com

Software:

AutoCAD | SketchUp | 3ds Max | Lumion

V-Ray | Photoshop

Presentation portfolio prepared for architecture and 3D visualization job applications.



Architectural Visualization

Clean, realistic presentation of architecture, materials, light and atmosphere.

Focus

- Architectural exterior visualization
- Interior visualization and composition
- Material setup, lighting and atmosphere
- 2D AutoCAD technical drawings for portfolio presentation
- 2D/3D architectural support and presentation graphics

Portfolio Content

- 01 Commercial Office Building - exterior visualization
- 02 Residential Apartment Complex - day and night exterior views
- 03 Open-plan Living Room - interior visualization
- 04 Technical Documentation - AutoCAD floor plans



PROJECT 01

Commercial Office Building

Commercial and service building | Exterior visualization

Scope: exterior visualization, lighting, materials and presentation composition

Views: golden-hour facade, aerial roof perspective and diagonal exterior shots

Goal: clean commercial presentation with stronger atmosphere and realistic landscaping





Commercial Office Building - golden-hour front view

Exterior visualization | wet asphalt / warm office lighting



Commercial Office Building - frontal composition

Exterior visualization | glass, wood facade, parking area



Commercial Office Building - left diagonal view

Exterior visualization | professional camera angle



Commercial Office Building - aerial roof view

Exterior visualization | roof and site layout

PROJECT 02

Residential Apartment Complex

Residential development | Day and night exterior visualization

Scope: exterior scenes, facade materials, street context and night lighting

Views: left diagonal, right diagonal, front elevation and night atmosphere

Goal: residential presentation with clear facade rhythm and stronger visual realism





Residential Apartment Complex - left diagonal view

Exterior visualization | warm daylight / street context



Residential Apartment Complex - right diagonal view

Exterior visualization | street corner composition



Residential Apartment Complex - front elevation

Exterior visualization | symmetrical composition



Residential Apartment Complex - night render

Exterior visualization | interior lights / moonlight atmosphere

PROJECT 03

Open-plan Living Room

Open-plan living room and kitchen | Interior visualization

Scope: interior composition, daylight, furniture, materials and decor presentation

Views: kitchen-living composition and diagonal living-room perspective

Goal: warm, clean interior presentation suitable for client communication





Open-plan Living Room - kitchen and dining composition

Interior visualization | warm daylight / Scandinavian style



Open-plan Living Room - diagonal living-room view

Interior visualization | furniture, window and lighting composition

PROJECT 04


Technical Documentation

AutoCAD 2D drawings | floor plans and dimensioned plans


Scope: clean black/gray technical linework.

Content: floor plans, room labels and dimensioned layouts.


Goal: show AutoCAD drafting and technical presentation skills.

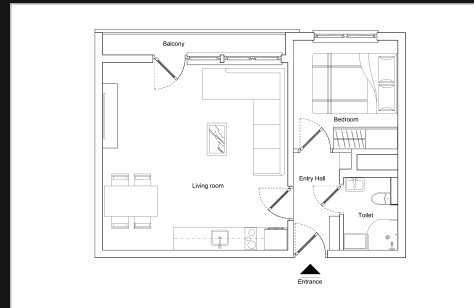


Floor plan 1:20

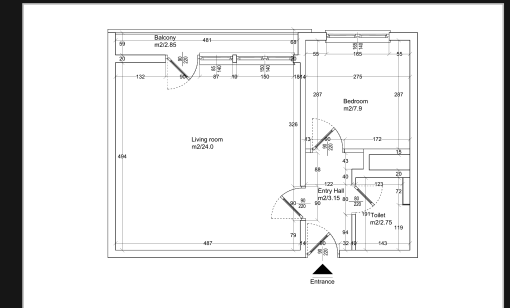

Dimensioned plan 1:20

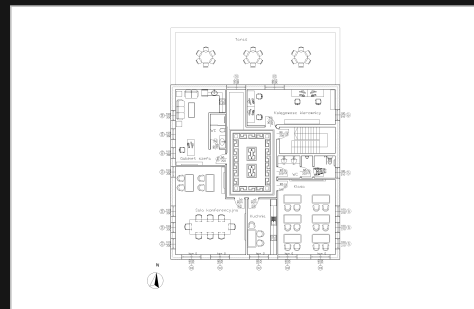

Attic floor plan 1:50

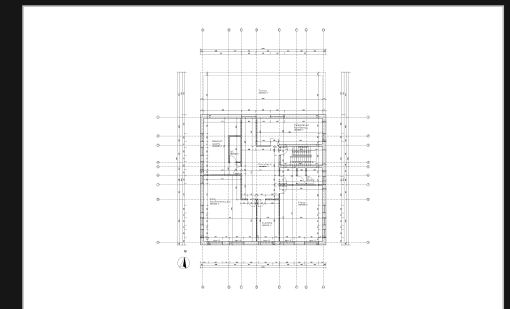


Measured attic plan 1:50

Apartment Floor Plan

SCALE 1:20

Black/gray linework | furniture layout | portfolio technical sheet

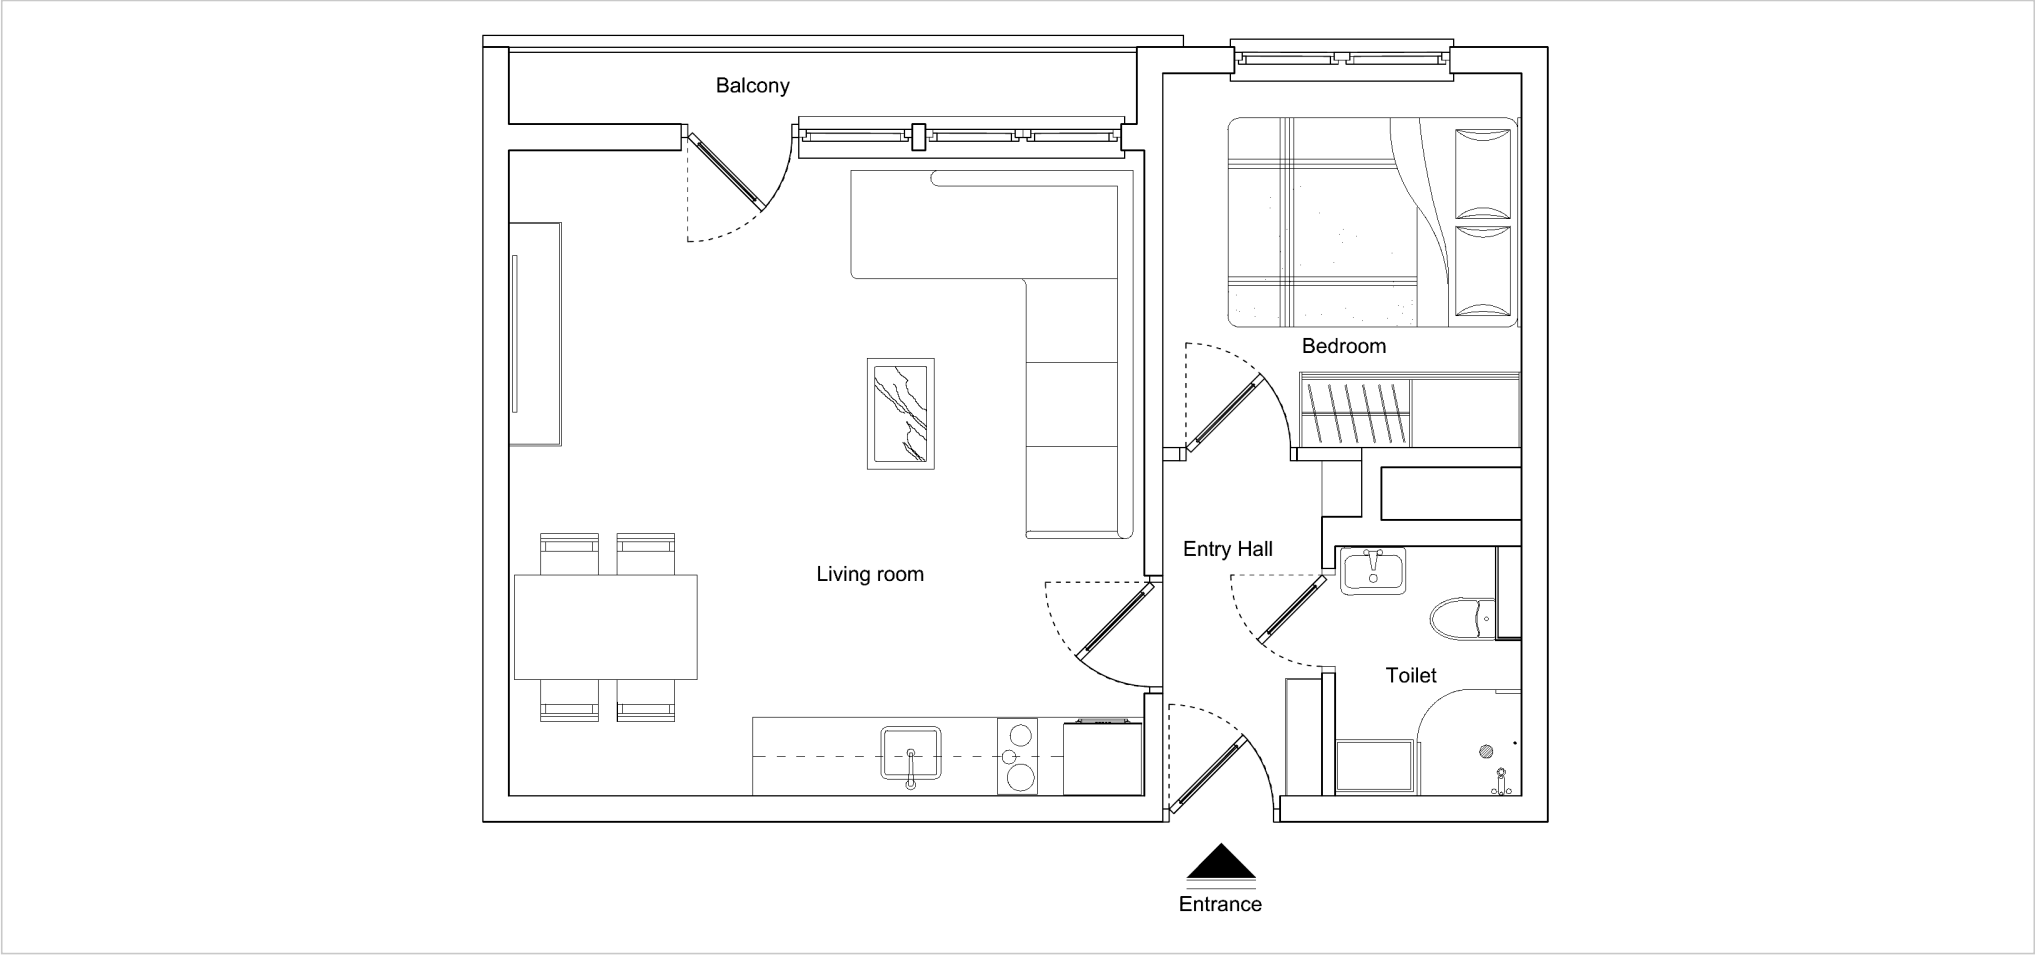


PROJECT	DRAWING	SCALE	SOFTWARE	AUTHOR
Apartment Interior Layout	Floor Plan	1:20	AutoCAD	Ruslan Ovezov

Apartment Dimensioned Floor Plan

SCALE 1:20

Black/gray linework | dimensions and room areas | portfolio technical sheet

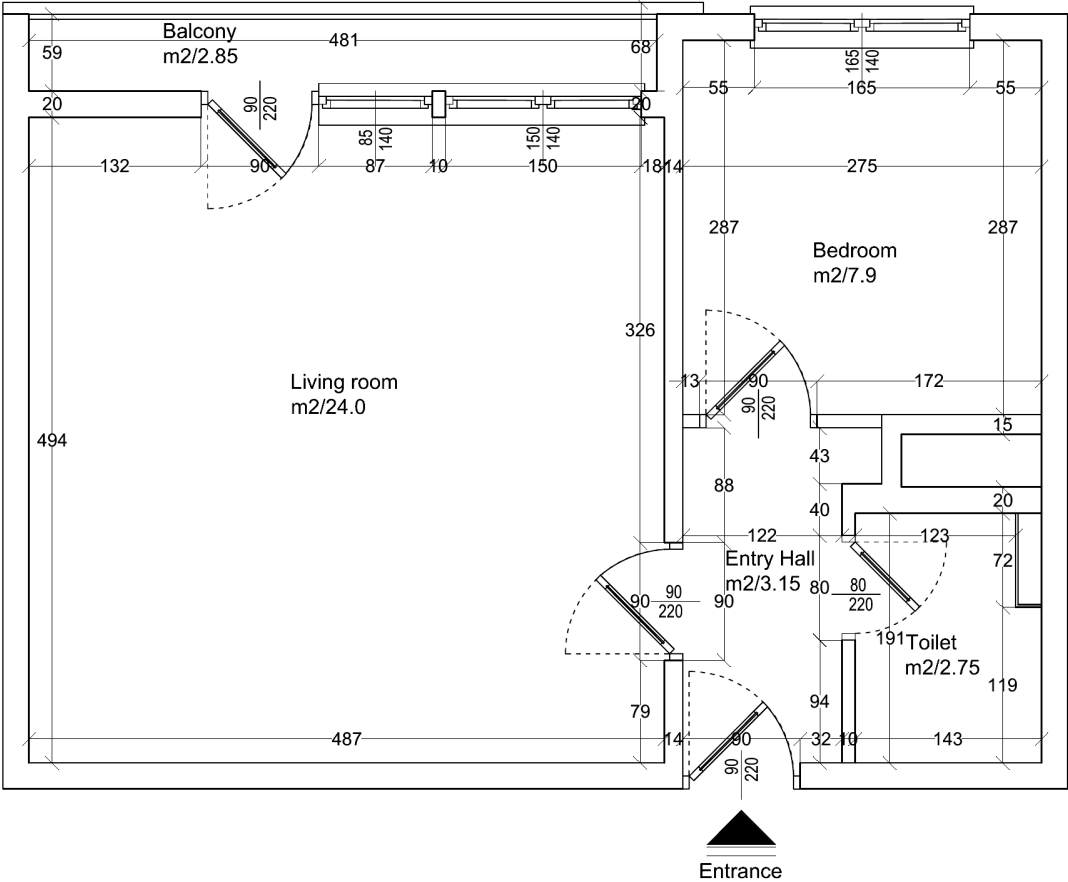


PROJECT	DRAWING	SCALE	SOFTWARE	AUTHOR
Apartment Interior Layout	Dimensioned Floor Plan	1:20	AutoCAD	Ruslan Ovezov

Attic floor plan

Attic floor plan | furniture and functional layout | portfolio technical sheet

SCALE 1:50

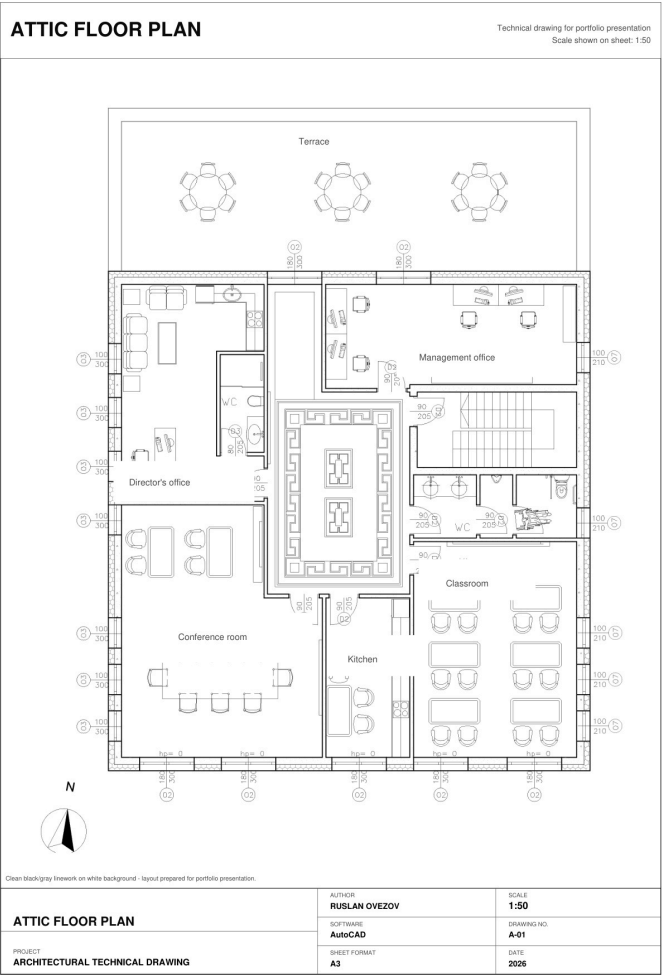

1:50

DRAWING SCALE

PROJECT
Office Building Concept

DRAWING
Attic floor plan


SCALE
1:50

SOFTWARE
AutoCAD

AUTHOR
Ruslan Ovezov

Attic floor plan - measured plan

Attic floor plan - measured 2D technical drawing

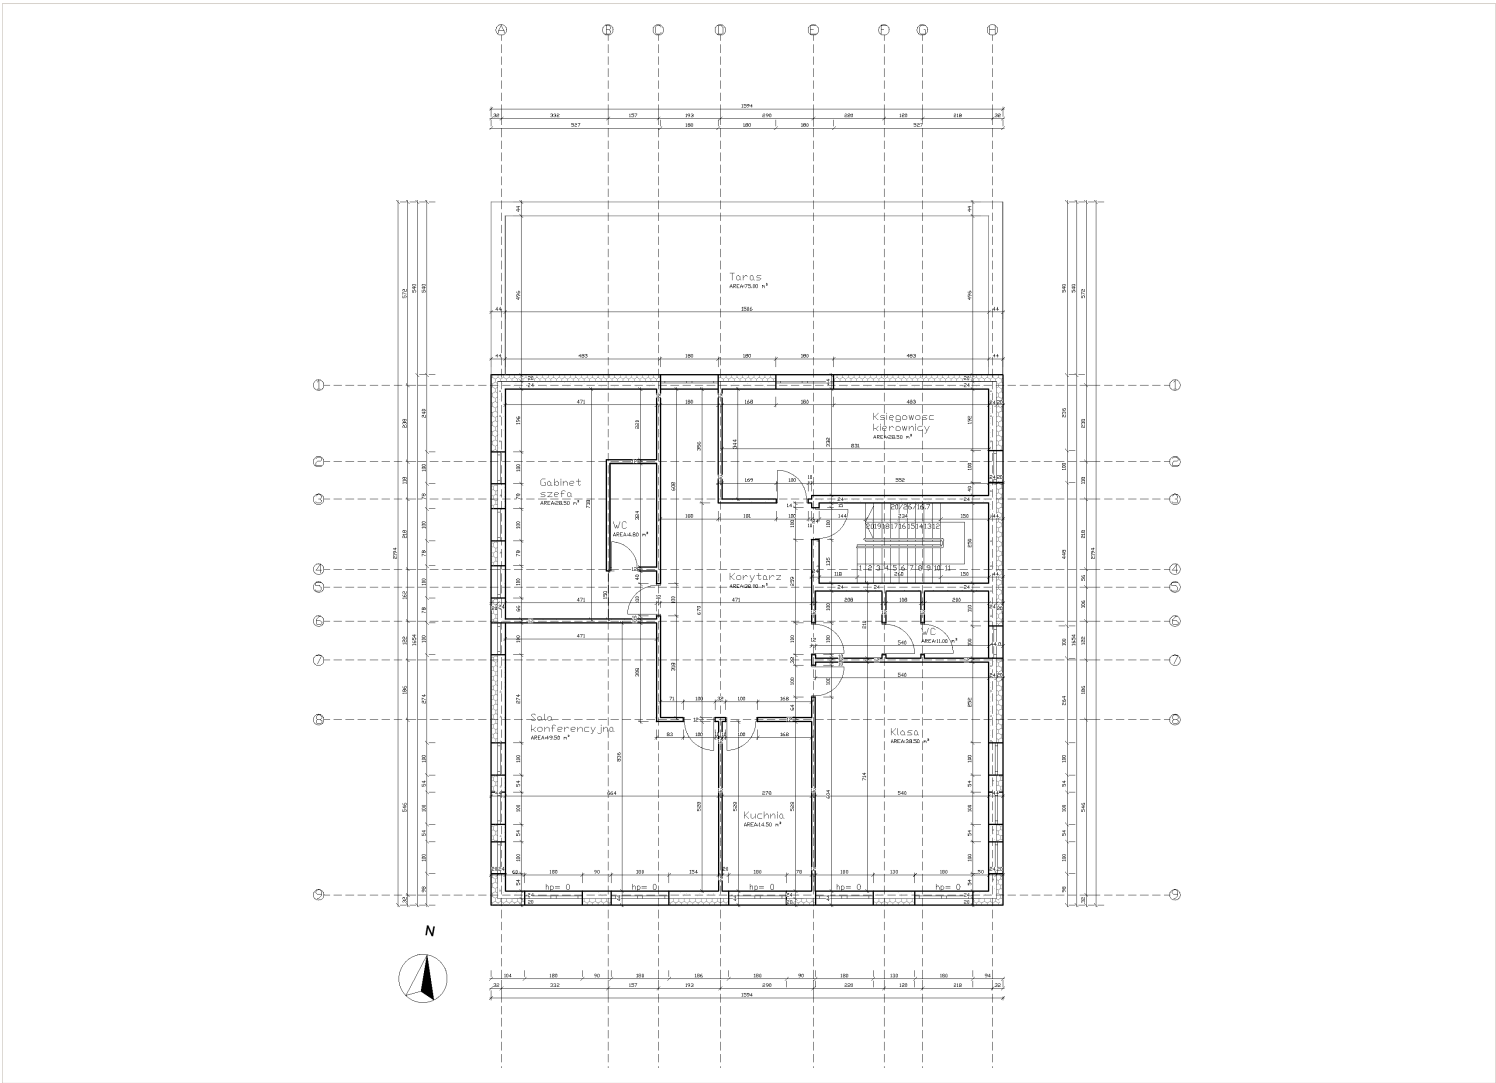

DRAWING SCALE

1:50

PROJECT	Office Building Concept
DRAWING	Dimensioned attic plan
SCALE	1:50
SOFTWARE	AutoCAD
AUTHOR	Ruslan Ovezov

Drawing scope

- functional floor layout
- walls, axes and dimensions
- room labels
- technical sheet preparation

Thank you

Ruslan Ovezov

Architect | Architectural Visualizer | 3D Artist

Lublin, Poland

+48 789 607 914

architectruslann@gmail.com

