

PORTFOLIO

RUSLAN OVEZOV

Architect | Architectural Visualizer | 3D Artist

Selected architectural visualization works

Exterior renders | Interior renders | Lighting | Post-production

Lublin, Poland

+48 789 607 914

architectruslann@gmail.com

Software:

AutoCAD | SketchUp | 3ds Max | Lumion

V-Ray | Photoshop

Presentation portfolio prepared for architecture and 3D visualization job applications.



Architectural Visualization


Clean, realistic presentation of architecture, materials, light and atmosphere.

Focus

- Architectural exterior visualization
- Interior visualization and composition
- Material setup, lighting and atmosphere
- 2D AutoCAD technical drawings for portfolio presentation
- 2D/3D architectural support and presentation graphics

Portfolio Content

- 01 Commercial Office Building - exterior visualization
- 02 Residential Apartment Complex - day and night exterior views
- 03 Modern Apartment Interior - living room, hallway, bathroom and bedroom
- 04 Technical Documentation - AutoCAD floor plans

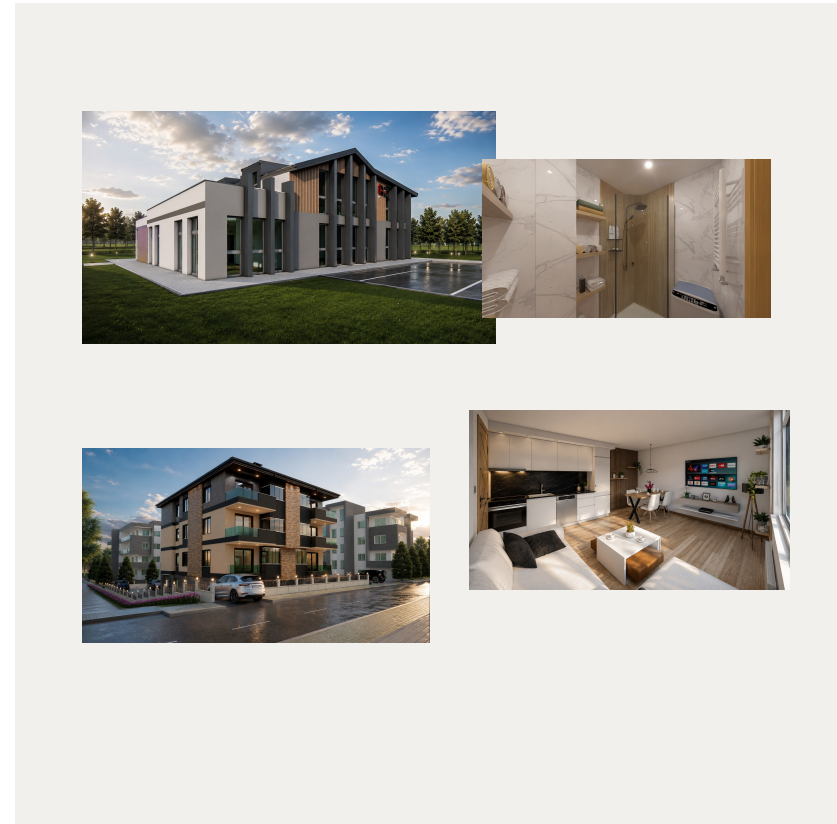

PROJECT 01

Commercial Office Building

Commercial and service building | Exterior visualization

Scope: exterior visualization, lighting, materials and presentation composition

Views: golden-hour facade, frontal view, aerial roof perspective and diagonal shots

Goal: clean commercial presentation with strong atmosphere and realistic landscaping





Commercial Office Building - golden-hour front view

Exterior visualization | wet asphalt / warm office lighting



Commercial Office Building - frontal composition

Exterior visualization | glass, wood facade, parking area



Commercial Office Building - left diagonal view

Exterior visualization | professional camera angle



Commercial Office Building - aerial roof view

Exterior visualization | roof and site layout



Commercial Office Building - sunset facade view

Exterior visualization | warm sunset atmosphere

PROJECT 02

Residential Apartment Complex

Residential development | Day and night exterior visualization

Scope: exterior scenes, facade materials, street context and night lighting

Views: left diagonal, right diagonal, front elevation and night atmosphere

Goal: residential presentation with clear facade rhythm and stronger visual realism





Residential Apartment Complex - left diagonal view

Exterior visualization | warm daylight / street context



Residential Apartment Complex - right diagonal view

Exterior visualization | street corner composition



Residential Apartment Complex - front elevation

Exterior visualization | symmetrical composition



Residential Apartment Complex - night render

Exterior visualization | interior lights / moonlight atmosphere

PROJECT 03


Modern Apartment Interior

Living room, kitchen, hallway, bathroom and bedroom | Interior visualization

Scope: interior composition, daylight, furniture, materials and decor presentation

Views: open-plan living area, hallway, bathroom and bedroom perspectives

Goal: warm, clean apartment presentation suitable for client communication

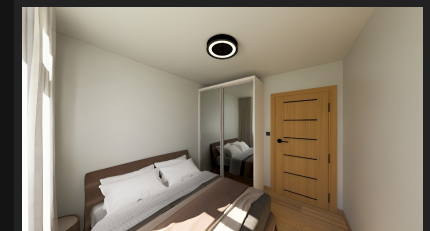



Open-plan Living Room - kitchen and dining composition

Interior visualization | warm daylight / Scandinavian style



Open-plan Living Room - diagonal living-room view

Interior visualization | furniture, window and lighting composition



Hallway - coat storage and wood panel wall

Interior visualization | hallway storage / warm wood lighting



Hallway - entrance view with wooden doors

Interior visualization | entrance zone / door rhythm



Bathroom - shower and laundry area

Interior visualization | marble surfaces / glass shower



Bathroom - vanity and shower view

Interior visualization | vanity / shower glass / wood accents



Bedroom - wardrobe view

Interior visualization | bed, wardrobe and neutral palette

**Bedroom - window view**

Interior visualization | daylight / curtains / calm atmosphere



Living room and kitchen - wide view

Interior visualization | living area / kitchen / dining space



Living and dining area

Interior visualization | TV wall / dining area / daylight

PROJECT 04




Technical Documentation

AutoCAD 2D drawings | floor plans and dimensioned plans

Scope: clean black/gray technical linework

Content: floor plans, room labels and dimensioned layouts


Goal: show AutoCAD drafting and technical presentation skills

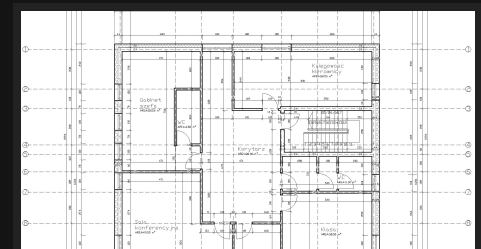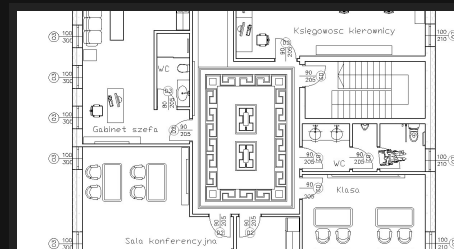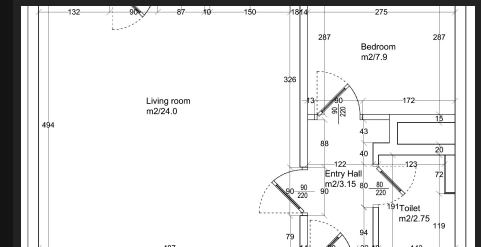

Apartment Floor Plan

SCALE 1:20

Black/gray linework | furniture layout | portfolio technical sheet

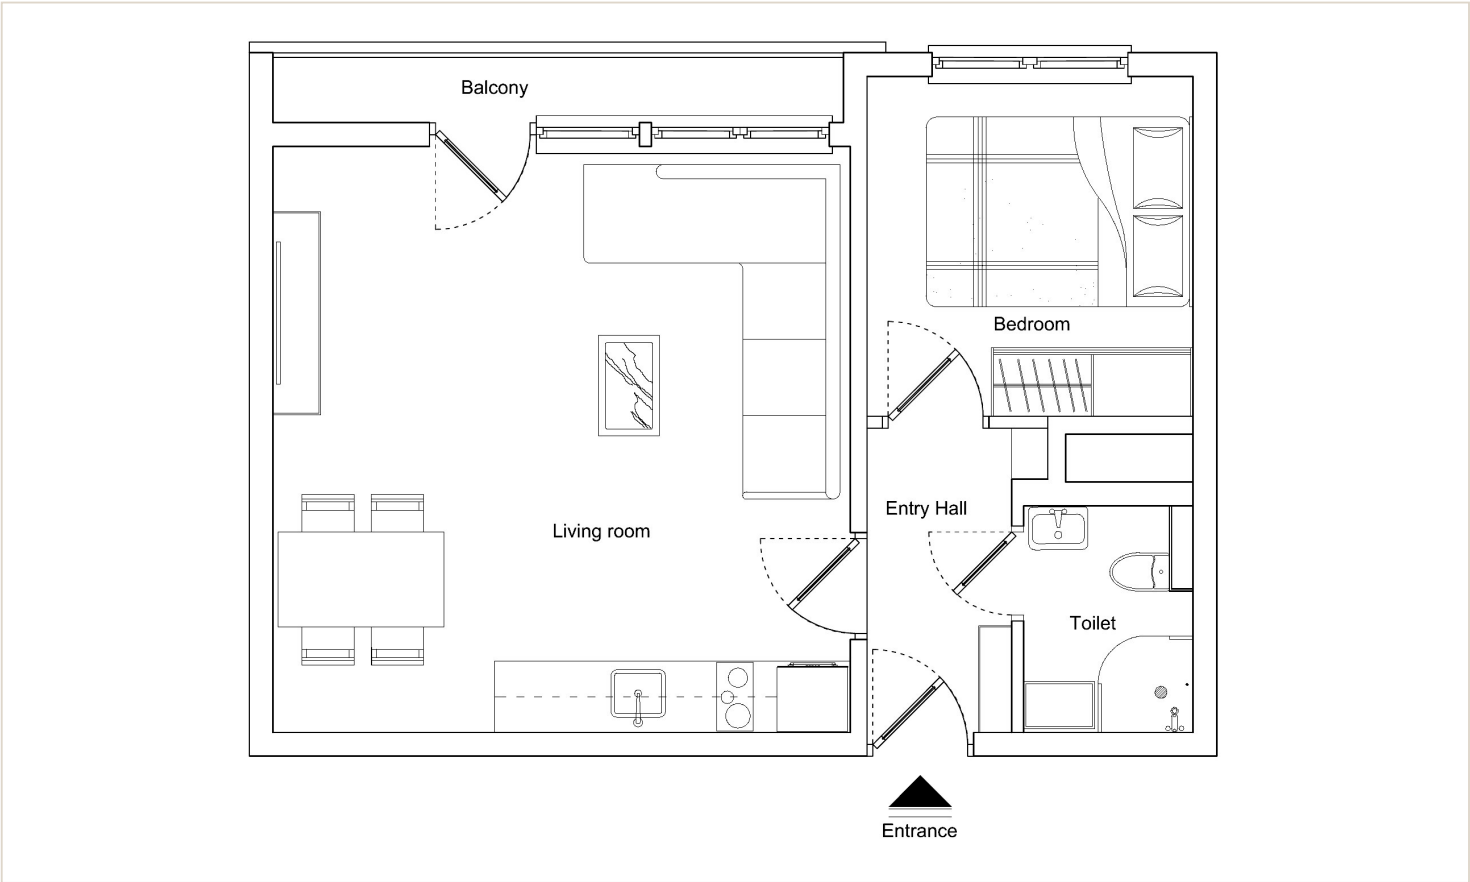


1:20
DRAWING SCALE

PROJECT	Apartment Interior Layout
DRAWING	Floor Plan
SCALE	1:20
SOFTWARE	AutoCAD
AUTHOR	Ruslan Ovezov

Apartment Dimensioned Floor Plan

SCALE 1:20

Black/gray linework | dimensions and room areas | portfolio technical sheet

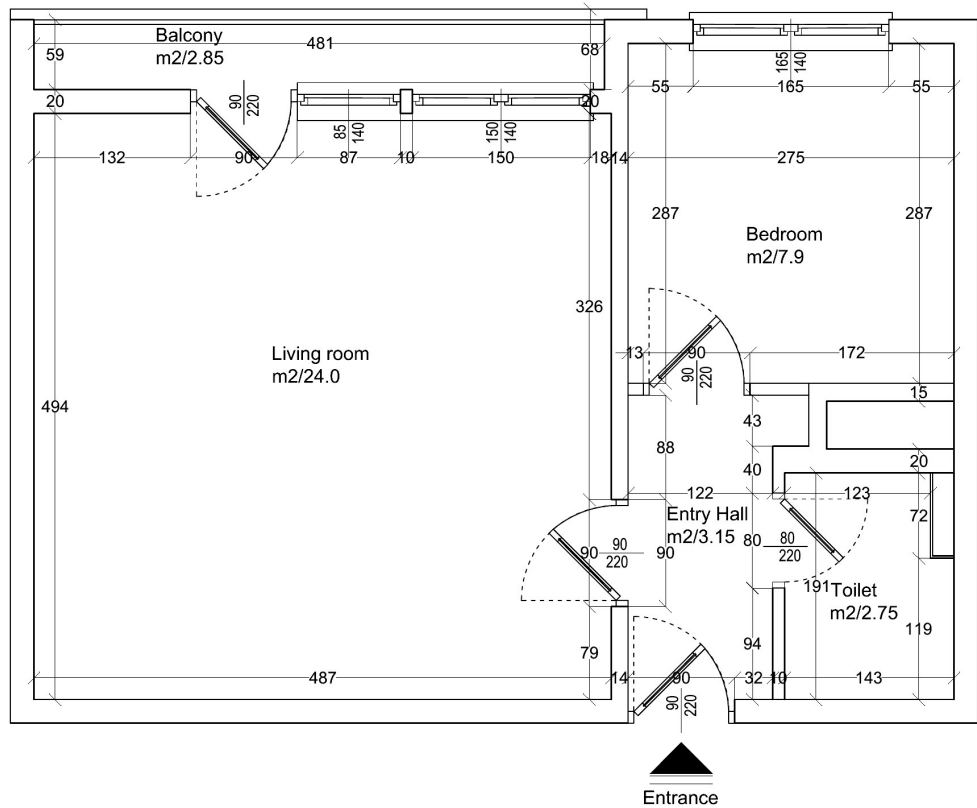


1:20
DRAWING SCALE

PROJECT	Apartment Interior Layout
DRAWING	Dimensioned Floor Plan
SCALE	1:20
SOFTWARE	AutoCAD
AUTHOR	Ruslan Ovezov

Attic floor plan

SCALE 1:50

Attic floor plan | furniture and functional layout | portfolio technical sheet

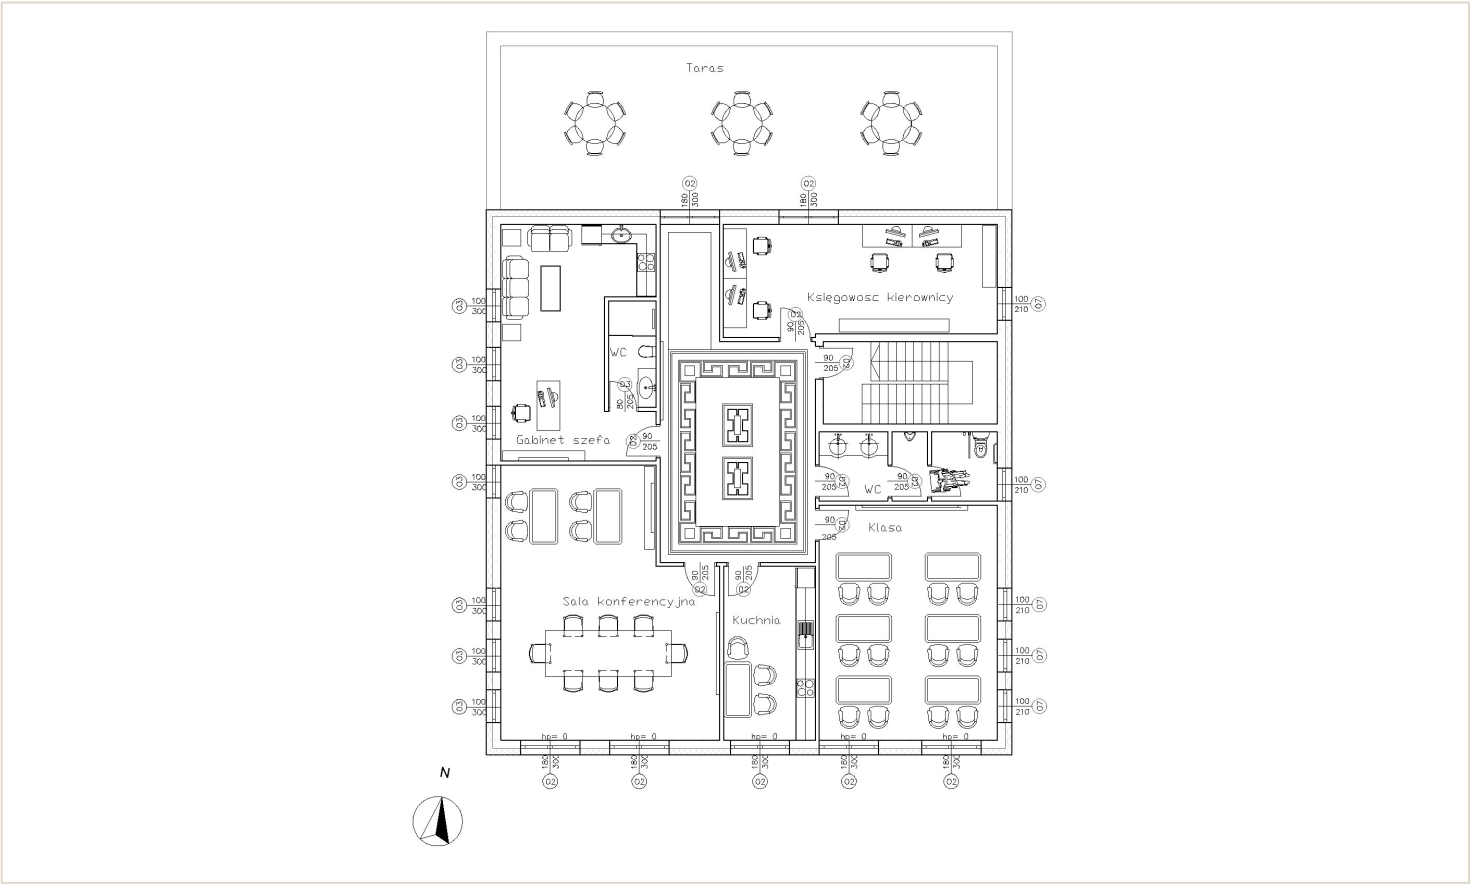

1:50


DRAWING SCALE

PROJECT	Office Building Concept
DRAWING	Attic floor plan
SCALE	1:50
SOFTWARE	AutoCAD
AUTHOR	Ruslan Ovezov

Attic floor plan - measured plan

SCALE 1:50

Attic floor plan - measured 2D technical drawing

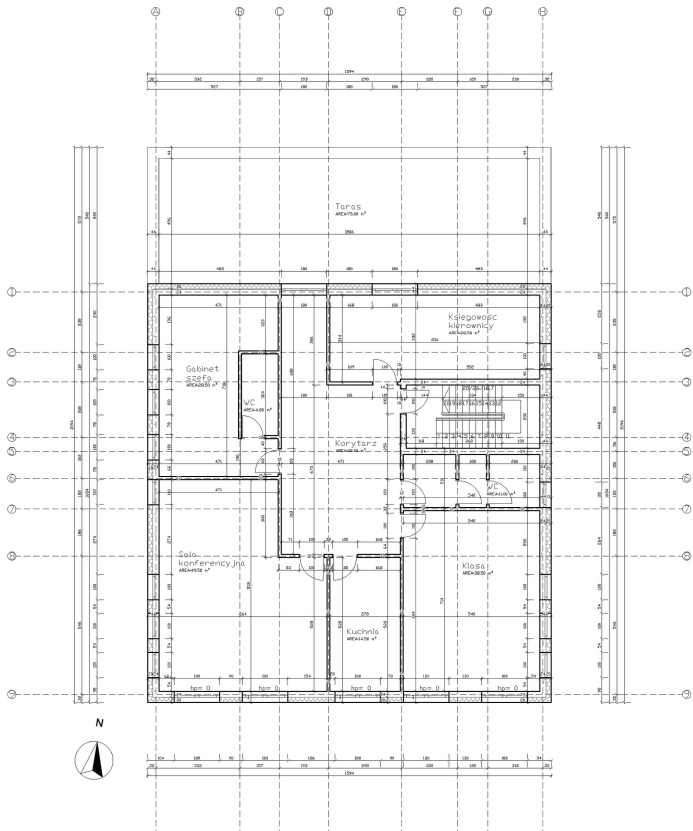

1:50
DRAWING SCALE

PROJECT	Office Building Concept
DRAWING	Dimensioned attic plan
SCALE	1:50
SOFTWARE	AutoCAD
AUTHOR	Ruslan Ovezov

Thank you

Ruslan Ovezov

Architect | Architectural Visualizer | 3D Artist

Lublin, Poland

+48 789 607 914

architectruslann@gmail.com

